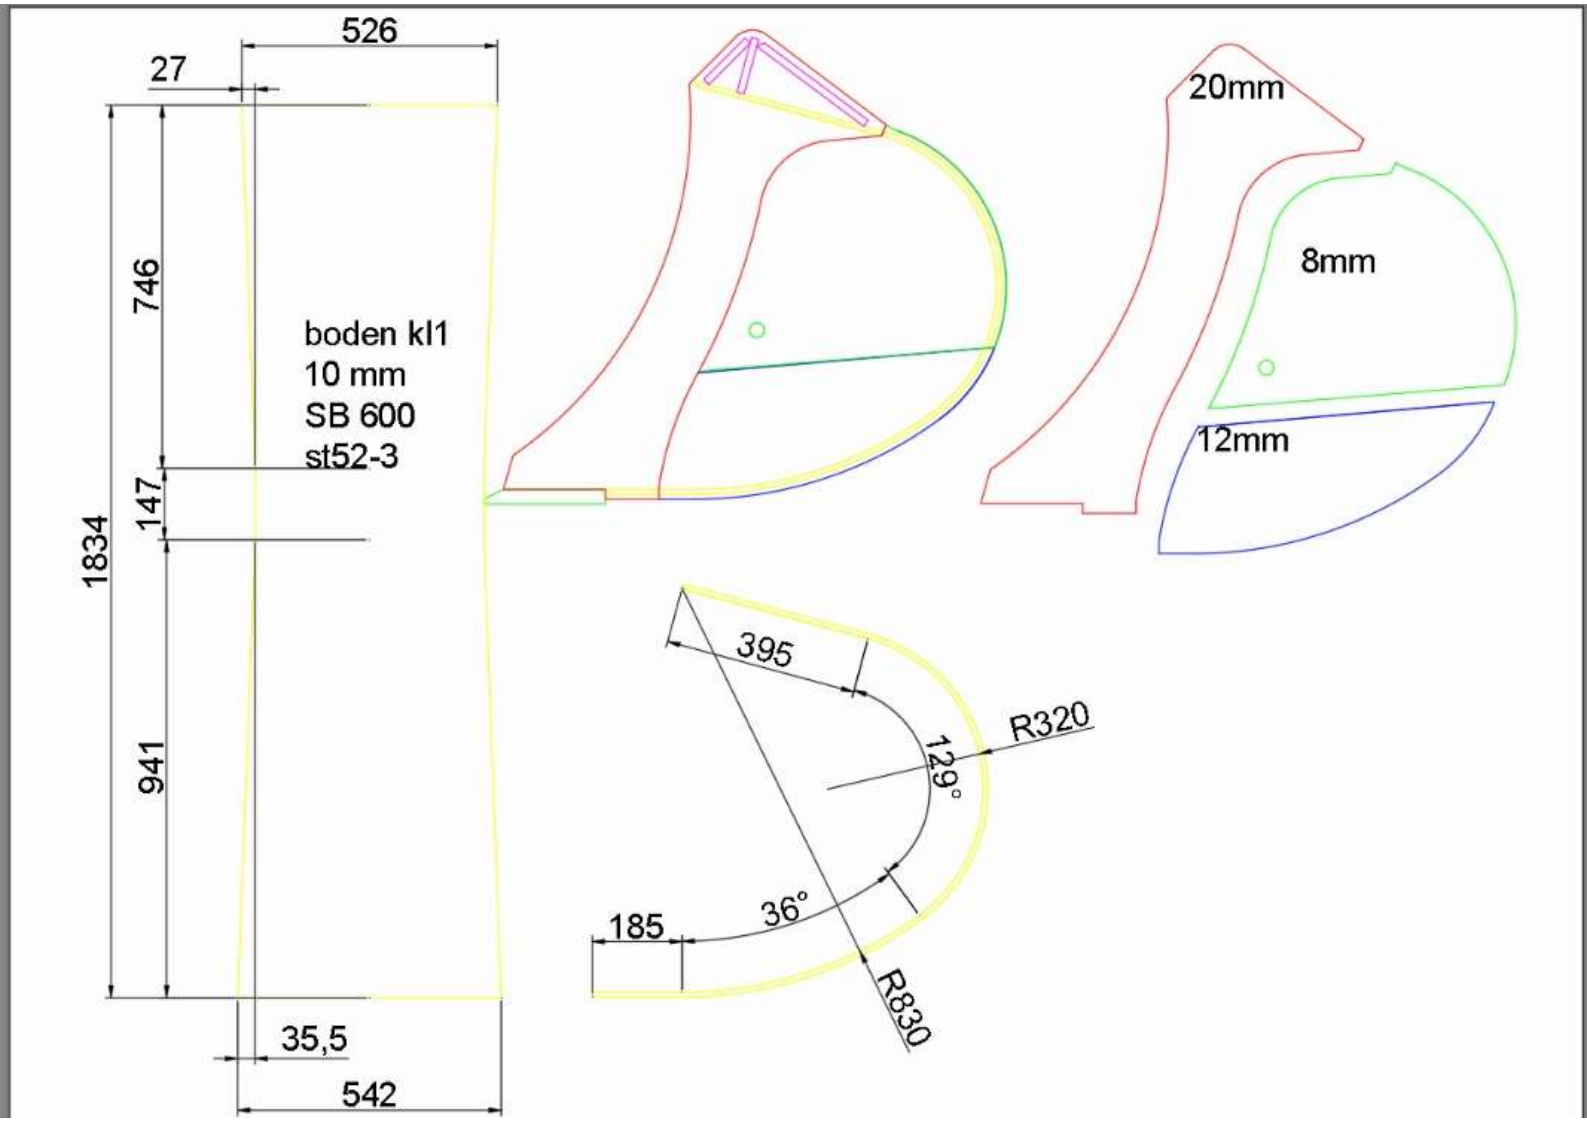
526
27
746
147
1834
941
35,5
542
boden kl1
10 mm
SB 600
st52-3
20mm
8mm
12mm
395
R320
129°
36°
185
R830